


Front View (Scale 1:5)

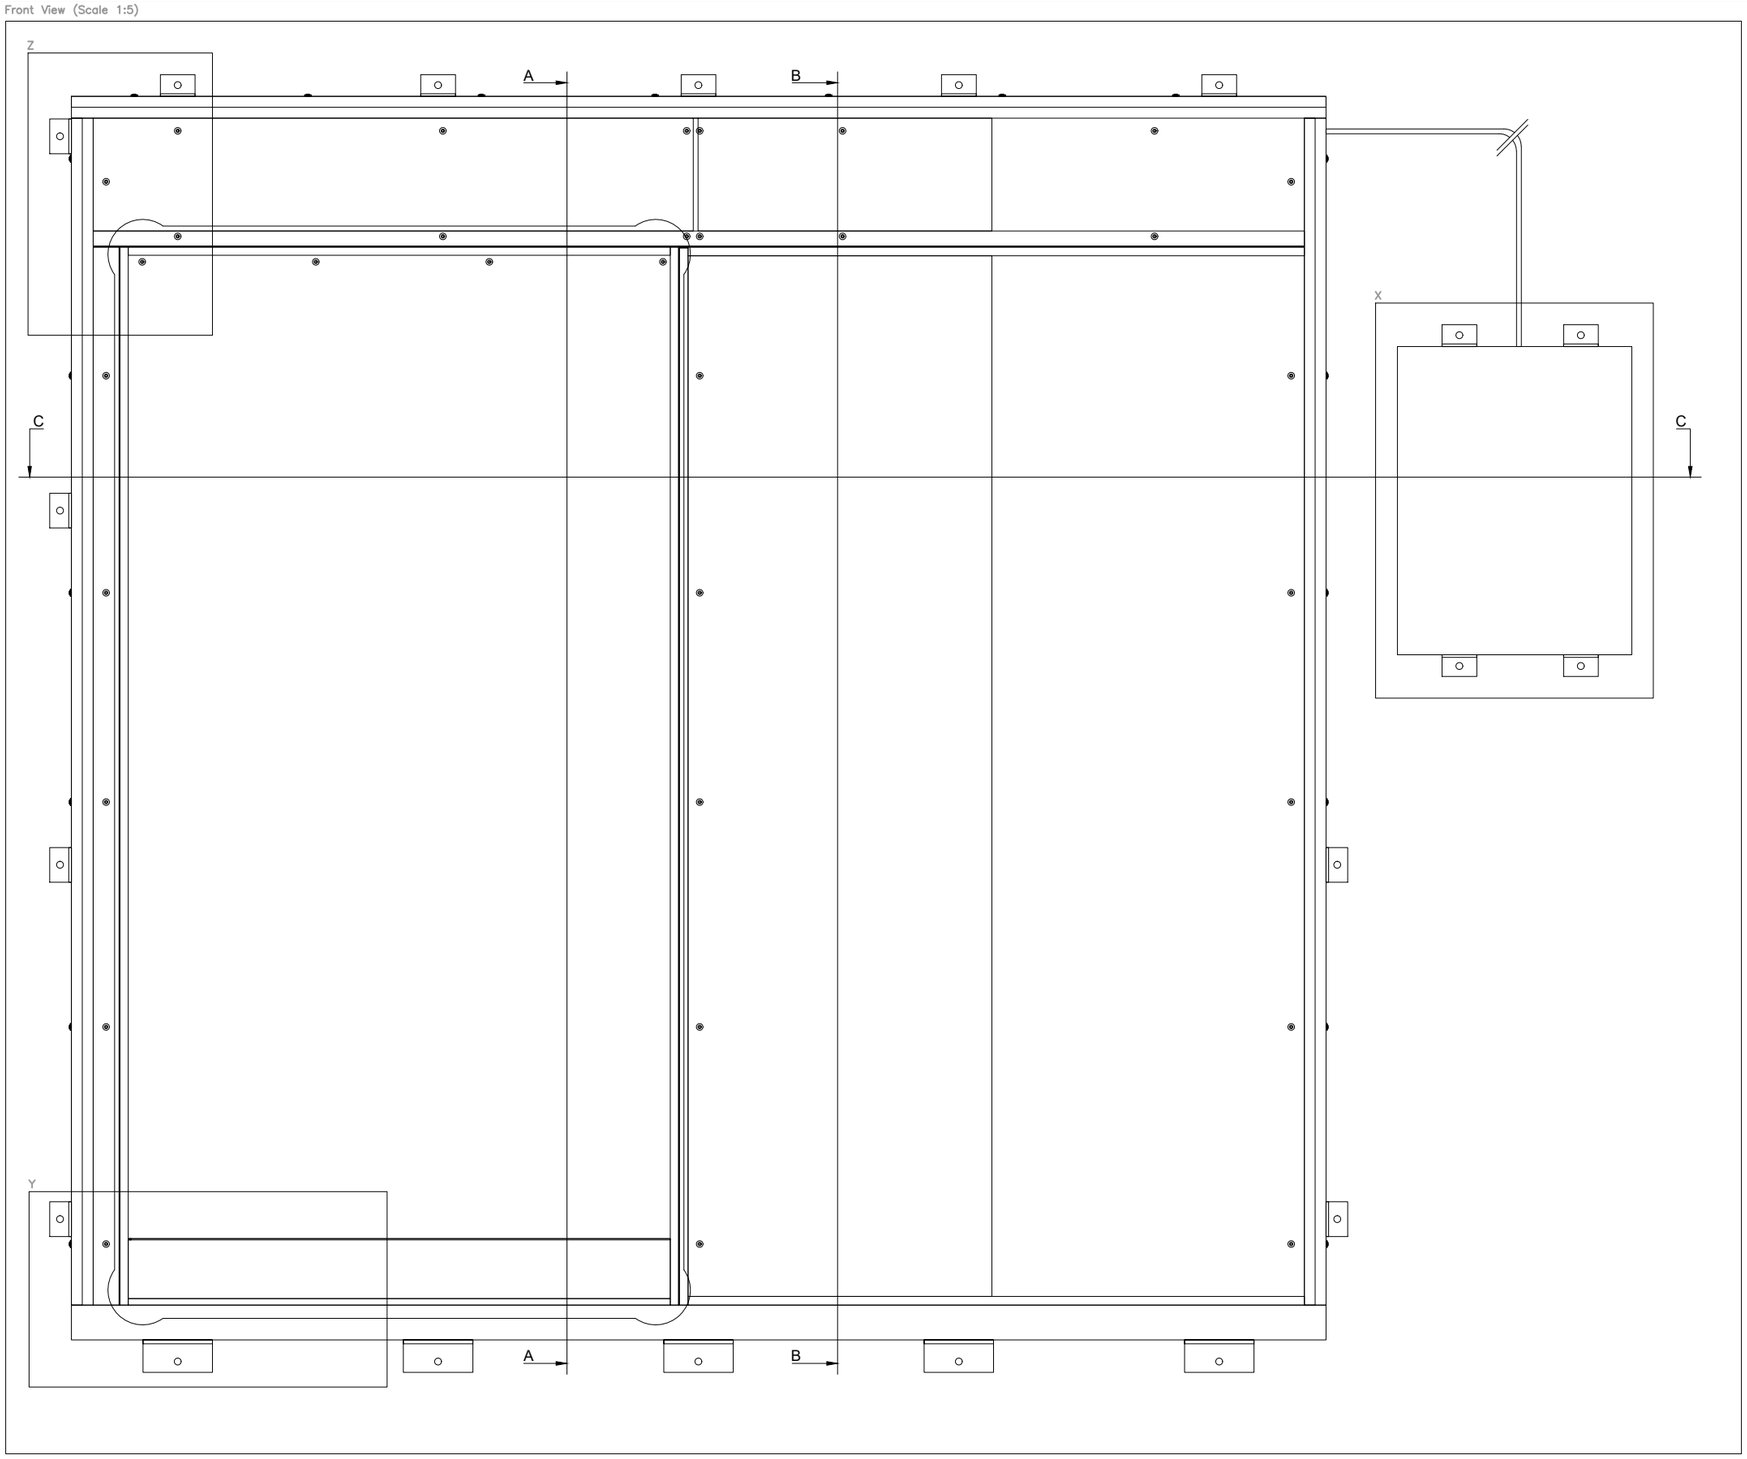


Side View A–A (Scale 1:5)

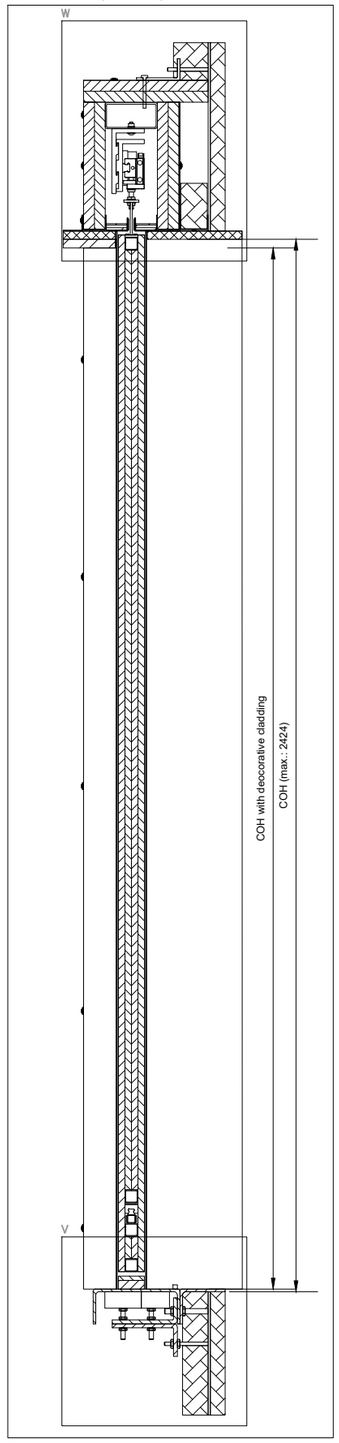

Side View B–B (Scale 1:5)

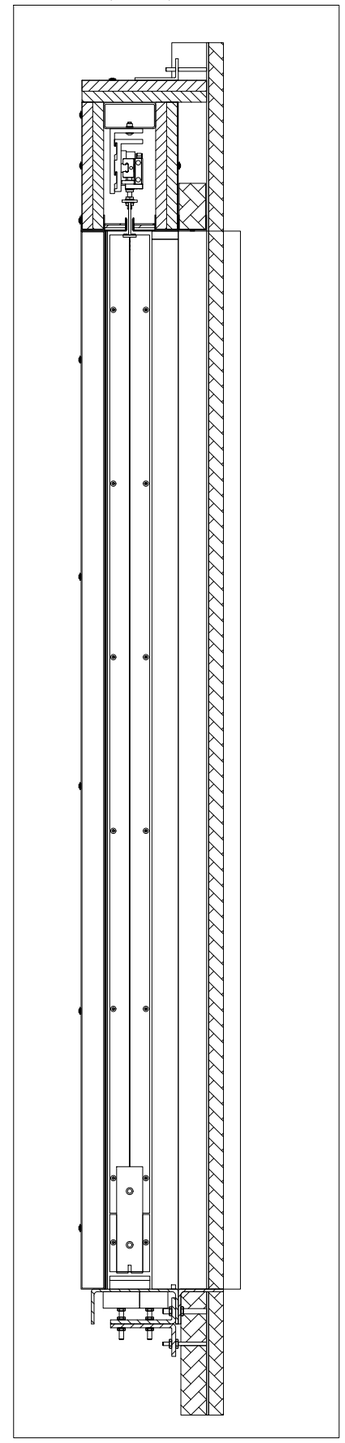

Top View C–C (Scale 1:5)

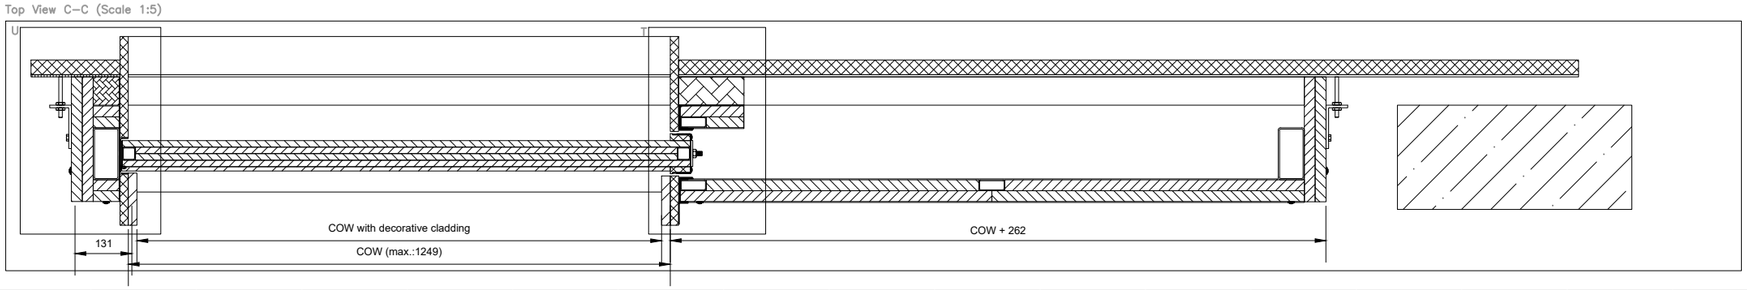


General remarks:
- The bulkhead's insulation system is shown only in idealized form and must be designed by the shipyard in accordance with applicable regulations.
-Decorative claddings are shown in various versions in the drawing; coordination regarding the final design must take place between the executing company and the supplier prior to the awarding of the contract.

Hatch pattern legend	
Material	Hatch style
Cladding	
SeaPan	
Bulkhead Insulation	
Thermax	
S235JR	


Projekt: 01	Zeichnung: 20.09.2020	S.Moazami		Werkstoff	
Auftrag: 0	Freigabe		Allgemeintoleranz ISO 2768 mK Oberflächen ISO 1302	Maßstab:	Klasse:
Position: 0	Bearbeitung/Überfl.	Status: S.Moazami	Schutzvermerk nach DIN ISO 16016 beachten.	Brandtestzeichnung A60 Innenschiebetür Innenseite	
Intern: 00	Extern:		LETHE exterior doors	Zeichnungsnummer: 260730 A60 Innenschiebetür	Rev.: 0
Bemerkungen:				Blatt: 1/1	Blattformat: A0
Ersatz für:				Ersetzt durch:	

Stand :


Detail W Type A (Scale 1:2)

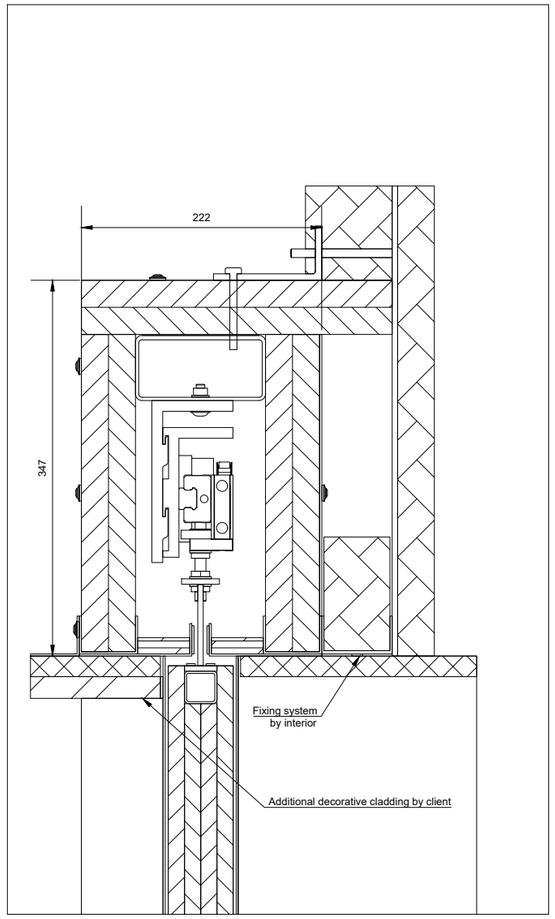


Detail V Type A (Scale 1:2)

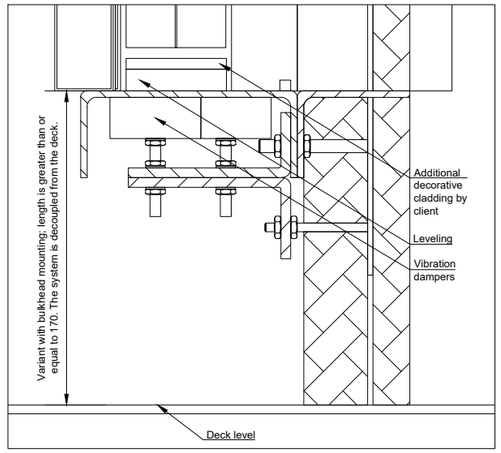


Detail V Type B (Scale 1:2)

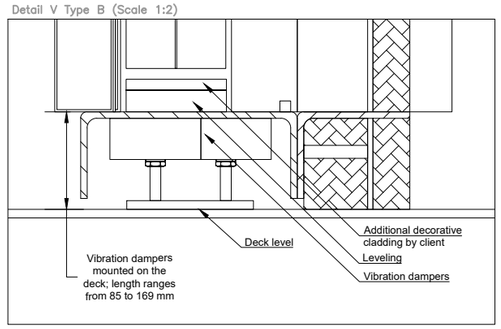


Detail V Type C (Scale 1:2)

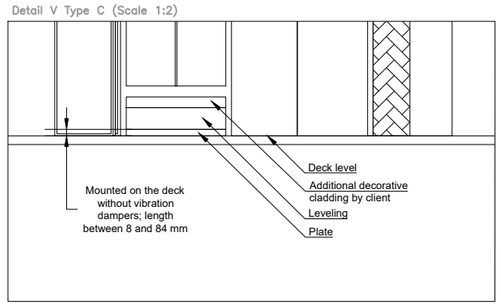


Detail U (Scale 1:2)

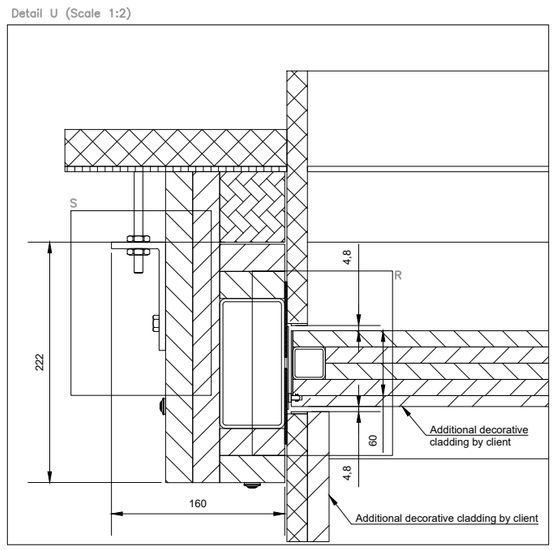


Detail T (Scale 1:2)

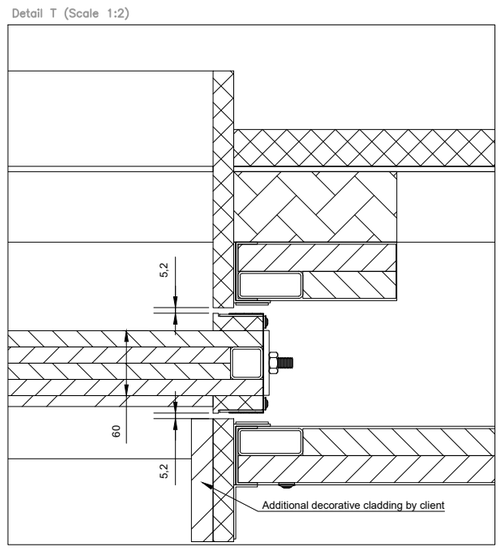


Detail Z Cut Out type K (Scale 1:2)

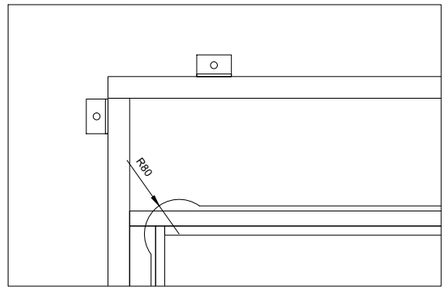


Detail Z Cut Out type V (Scale 1:2)

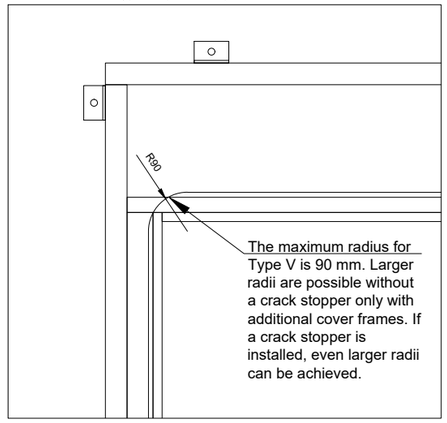


Detail S (Scale 1:1)

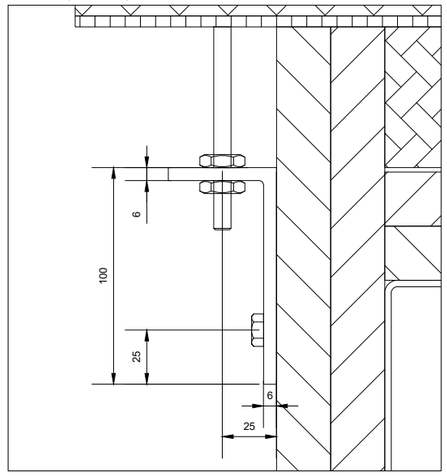


Detail R (Scale 1:1)

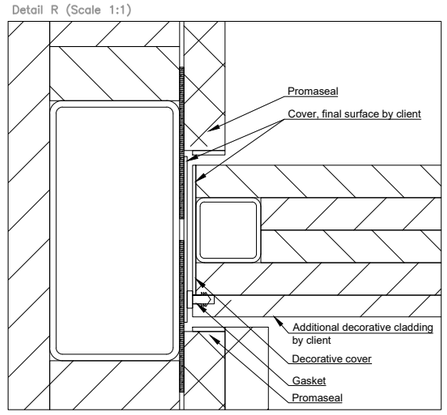


Detail Z Front View with Hose Port (Scale 1:5)

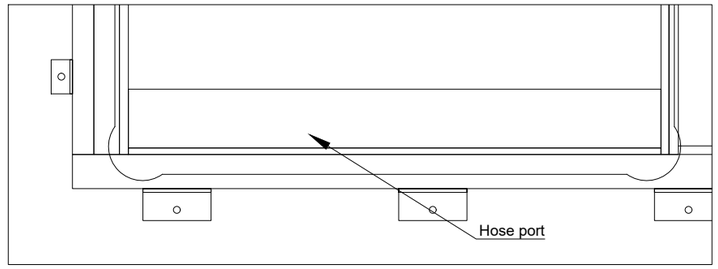

Detail Z Front View without Hose Port (Scale 1:5)

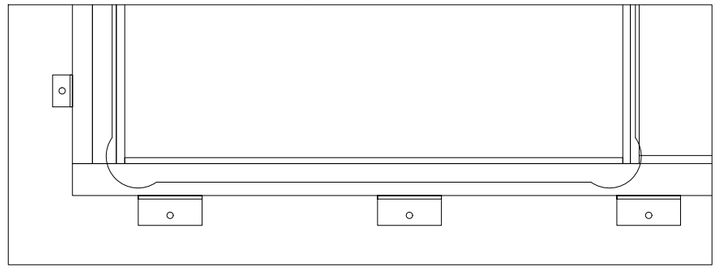

Detail X Front View Control Cabinet (Scale 1:5)

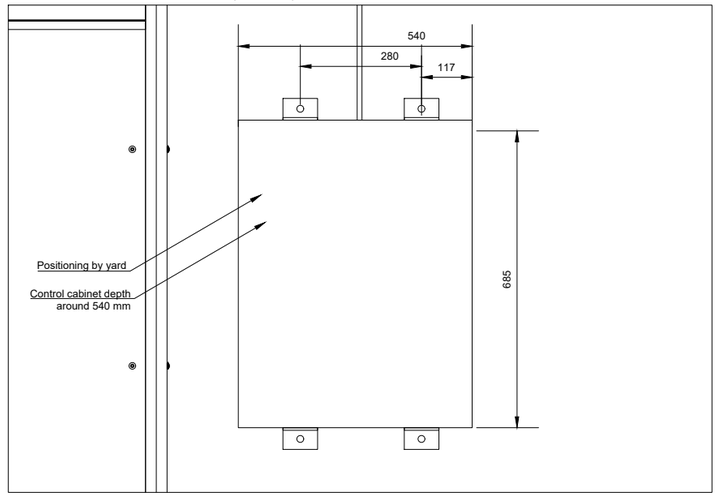

General remarks:
- The bulkhead's insulation system is shown only in idealized form and must be designed by the shipyard in accordance with applicable regulations.
-Decorative claddings are shown in various versions in the drawing; coordination regarding the final design must take place between the executing company and the supplier prior to the awarding of the contract.

Hatch pattern legend	
Material	Hatch style
Cladding	
SeaPan	
Bulkhead Insulation	
Thermax	
S235JR	

Projekt: 01
Auftrag: 0
Position: 0
Intern / Extern
Baugruppe: 00
Zeichnung: 20.08.2024 S.Moazami
Freigabe
Bearbeitung/Datum: -
Status: S.Moazami
Allgemeintoleranz ISO 2768 mK, Oberflächen: ISO 1302
Schutzvermerk nach DIN ISO 16016 beachten.
Werkstoff
Maßstab / Maßstab: Klasse
Brandtestzeichnung
A60 Innenschiebetür Innenseite
LETHE exterior doors
Zeichnungsnummer: 260730 A60 Innenschiebetür
Rev.: 0
Blattformat: A0
Blatt: 1/1
Erstellt für
Erstellt durch

Stand :